



Republika e Kosovës
Republika Kosova-Republic of Kosova
Qeveria -Vlada-Government

Ministria e Mjedisit dhe Planifikimit Hapësinor /Ministarstvo Sredine i Prostornog Planiranja/Ministry of Environment and Spatial Planning
AGJENCIA KADASTRALE E KOSOVËS/ KATASTARSKA AGENCIJA KOSOVA/ KOSOVA CADASTRAL AGENCY

Zyra kadastrale komunale / Opštinska katastarska kancelarija: Ferizaj

Nr. i njësisë kadastrale / Br. katastarske jedinice : 01024-0


Zona kadastrale / Katastarska zona: Greme

Numri i lëndës / Broj predmeta: _____

Lloji i njësisë kadastrale / Vrsta katastarske jedinice : Parcel

Shkalla e zvoglimit / Razmera plana : 1:750

Nr	Y	X	H	Kodi	Përshkrimi	Burimi
PK1	7515395.663	4692703.039	616.307	11	Monoment	PM
1	7515345.371	4686678.245	583.330	2	Shufër Metalike	PM
2	7515396.826	4686652.22	583.584	2	Shufër Metalike	PM
3	7515394.901	4686641.071	584.181	2	Shufër Metalike	PM
4	7515389.535	4686630.044	584.867	2	Shufër Metalike	PM
5	7515332.953	4686658.318	583.998	2	Shufër Metalike	PM
37609	7515364.497	4686583.558	584.517	2	Shufër Metalike	PM
37610	7515390.068	4686631.034	584.867	2	Shufër Metalike	PM
37611	7515400.439	4686652.573	583.984	2	Shufër Metalike	PM
41568	7515409.14	4686686.121	582.588	2	Shufër Metalike	PM
41569	7515383.23	4686690.322	582.578	2	Shufër Metalike	PM
41570	7515359.831	4686704.872	582.512	2	Shufër Metalike	PM
41977	7515341.19	4686670.545	583.711	2	Shufër Metalike	PM
41978	7515333.329	4686658.755	584.052	2	Shufër Metalike	PM
41979	7515326.069	4686650.306	584.312	2	Shufër Metalike	PM
41980	7515303.718	4686631.878	584.565	2	Shufër Metalike	PM
41985	7515403.64	4686671.542	582.948	2	Shufër Metalike	PM

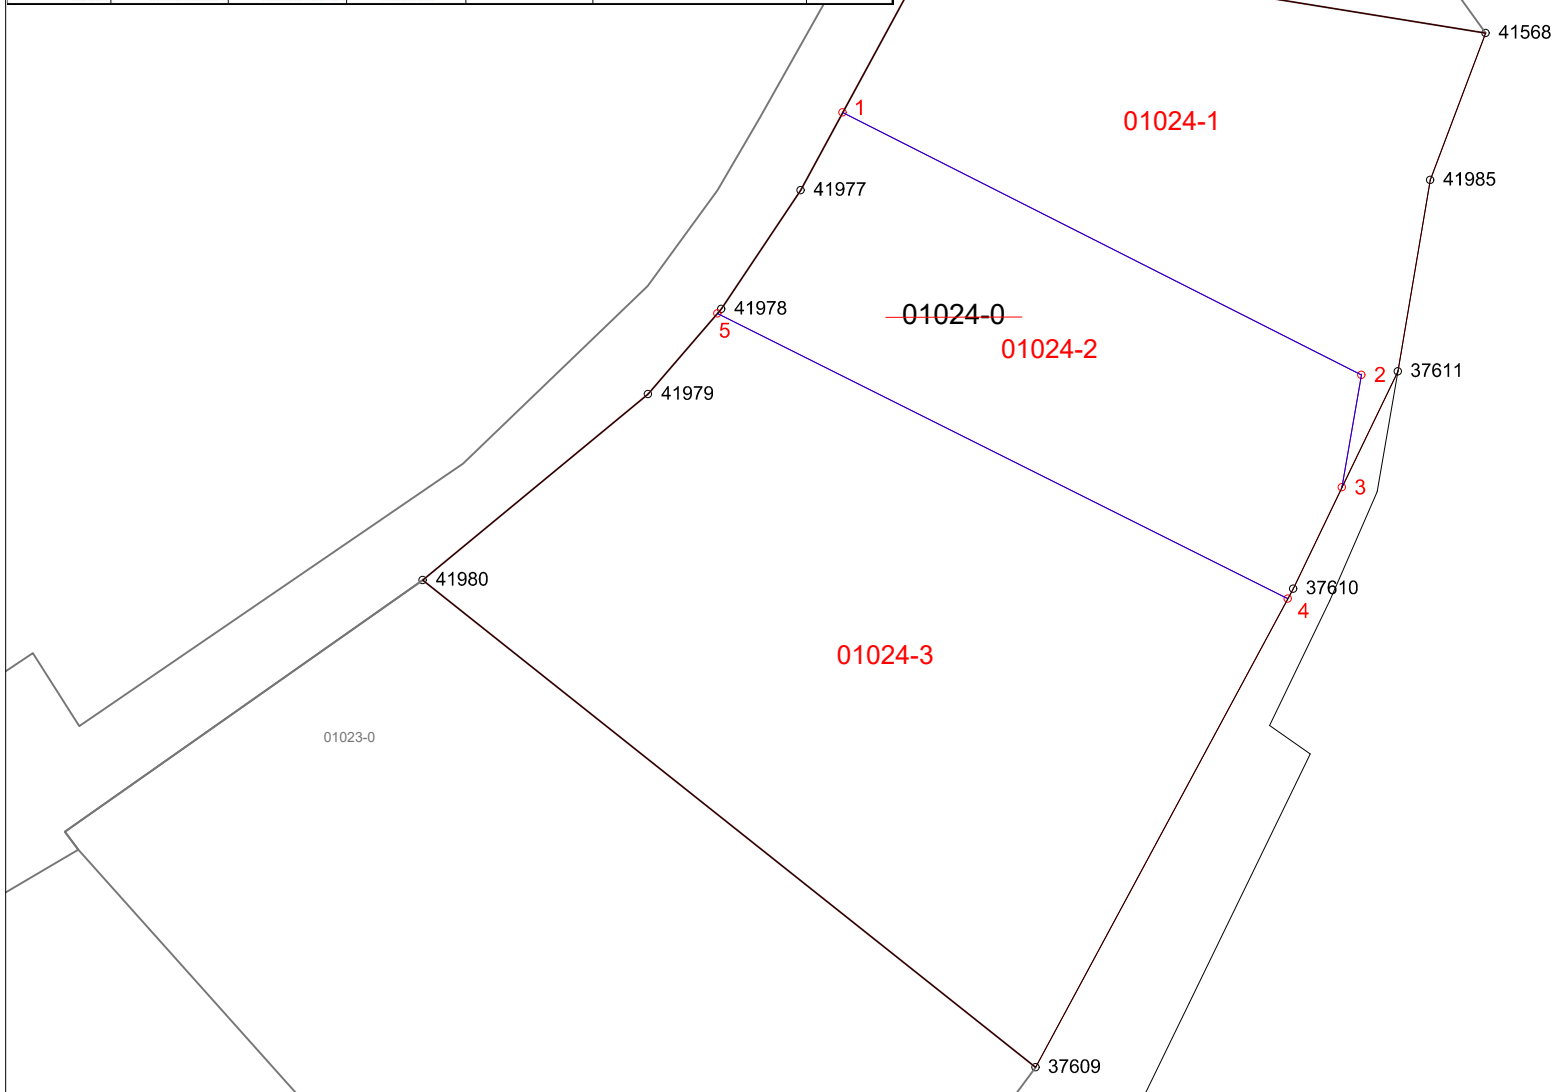

Rilevoi / Snimio: LIRIDON SEJDIU
(emri dhe mbiemri i gjeodetit/kompanisë/ ime i prezime geodeta/ kompanije)

Aprovoi / Usvojio: _____
(emri dhe mbiemri i përsorit zyrtar/ ime i prezime shërbëtorit)

Nr. i licencës / Br. licence: 140

V.V.

Nënshkrimi / Potpis: _____

Nënshkrimi / Potpis: _____

Data e rilevimit / Datum snimanja: 24.10.2025

Data e aprovimit / Datum usvajanja: _____