



**Republika e Kosovës**  
**Republika Kosova-Republic of Kosova**  
*Qeveria -Vlada-Government*

*Ministria e Mjedisit dhe Planifikimit Hapësinor /Ministarstvo Sredine i Prostornog Planiranja/Ministry of Environment and Spatial Planning*  
AGJENCIJA KADASTRALE E KOSOVËS/ KATASTARSKA AGECIJA KOSOVA/ KOSOVA CADASTRAL AGENCY

Zyra kadastrale komunale / Opštinska katastarska kancelarija: Ferizaj

Nr. i njësisë kadastrale / Br. katastarske jedinice : 03400-0

Zona kadastrale / Katastarska zona: \_\_\_\_\_ Greme

Numri i lëndës / Broj predmeta:

Lloji i njësisë kadastrale / Vrsta katastarske jedinice :


## Greme

## Parcel

Shkalla e zvoglimit / Razmra plana :

1:750

Nr	Y	X	H	Kodi	Përkrimi	Burimi
PK1	7515395.663	4692703.039	616.307	11	Monoment	PM
26222	7514481.417	4686625.242	587.586	2	Shufér Metalike	PM
26223	7514470.817	4686625.163	587.554	2	Shufér Metalike	PM
26224	7514459.967	4686632.063	587.573	2	Shufér Metalike	PM
28813	7514505.722	4686494.467	591.288	2	Shufér Metalike	PM
28814	7514530.022	4686503.376	591.379	2	Shufér Metalike	PM
28866	7514470.150	4686602.509	588.329	2	Shufér Metalike	PM
28868	7514487.046	4686608.283	587.637	2	Shufér Metalike	PM
28869	7514494.825	4686584.344	588.393	2	Shufér Metalike	PM
28870	7514499.774	4686564.254	589.091	2	Shufér Metalike	PM
28871	7514503.184	4686555.155	589.506	2	Shufér Metalike	PM
28872	7514503.184	4686555.145	589.506	2	Shufér Metalike	PM
28873	7514503.524	4686554.545	589.565	2	Shufér Metalike	PM
28874	7514507.354	4686547.755	589.966	2	Shufér Metalike	PM
28875	7514517.393	4686527.855	590.815	2	Shufér Metalike	PM
28876	7514510.193	4686523.306	590.781	2	Shufér Metalike	PM
28877	7514496.743	4686519.987	590.760	2	Shufér Metalike	PM
28878	7514495.233	4686528.076	590.703	2	Shufér Metalike	PM
28879	7514492.013	4686539.106	590.197	2	Shufér Metalike	PM
28880	7514481.889	4686567.022	591.376	2	Shufér Metalike	PM
28881	7514481.060	4686569.307	589.319	2	Shufér Metalike	PM
28882	7514470.967	4686600.137	588.421	2	Shufér Metalike	PM
38854	7514520.723	4686522.785	590.913	2	Shufér Metalike	PM
38857	7514498.063	4686514.967	590.604	2	Shufér Metalike	PM
38858	7514497.790	4686516.010	590.564	2	Shufér Metalike	PM

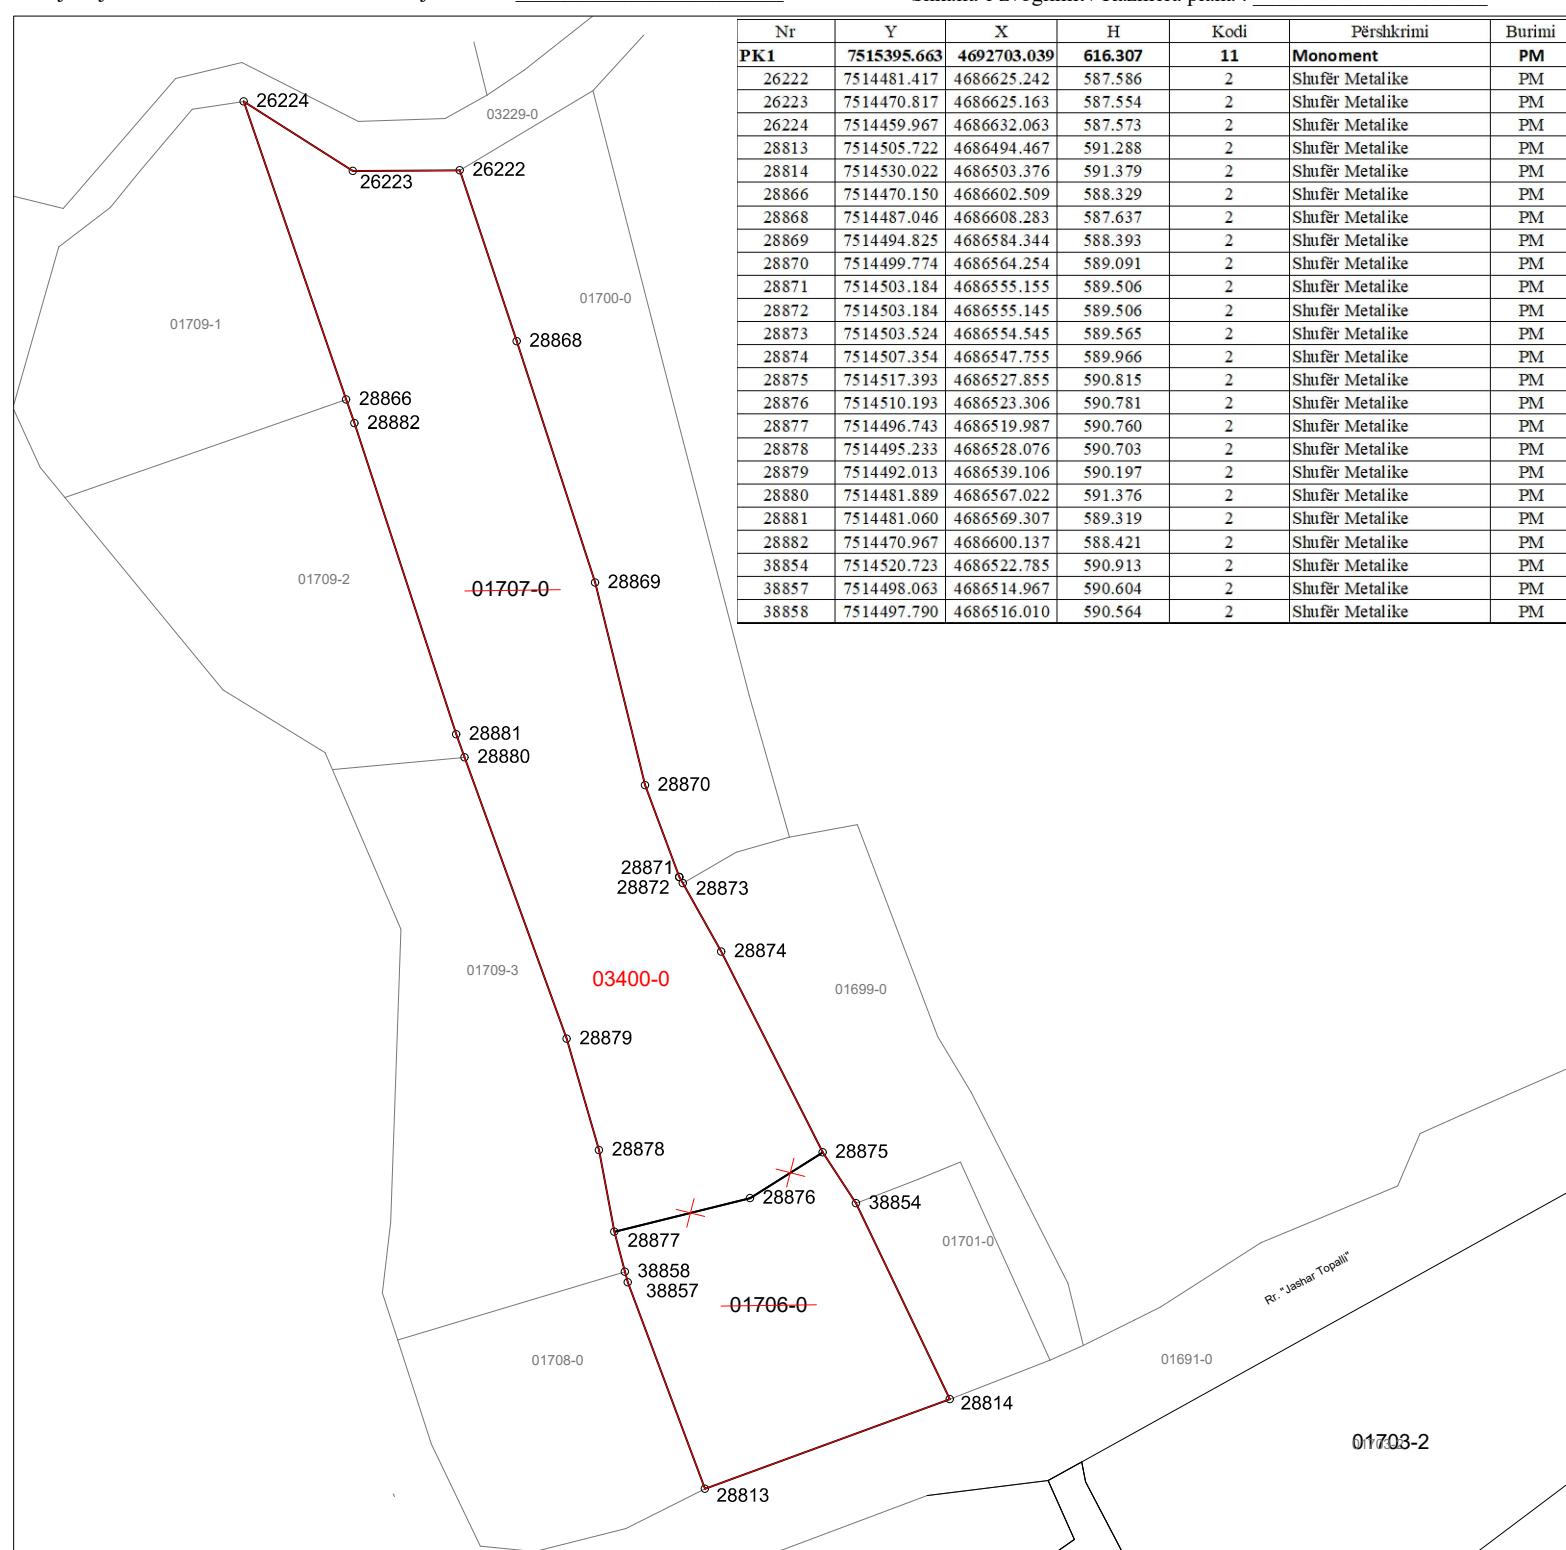

Rilevoi / Snimio: LIRIDON SEJDIU  
(emri dhe mbiemri i gjydetit/kompanisë/ ime i prezime geodeta/ kompanije)

Aprovoi / Usvojio: \_\_\_\_\_  
(emri dhe mbiemri i përsonit zyrtar/ ime i prezime sluzbenog lica)

Nr. i licencës / Br. licence: 140

V.V.

Nënshtkrimi / Potpis:

Nënshkrimi / Potpis:

Nënshtkimi / Potpis: \_\_\_\_\_

Datum emisji / Datum emigracji: 24.10.2025

Data e aprovimit / Datum usvajanja: