



REPUBLIKA E KOSOVËS / REPUBLIKA KOSOVA / REPUBLIC OF KOSOVO

QEVERTA E KOSOVËS / VLADA KOSOVA / GOVERNMENT OF KOSOVA

MINISTRIA E MJEDISIT, PLANIFIKIMIT HAPËSINOR DHE INFRASTRUKTURËS
MINISTARSTVO ŽIVOTNE SREDINE, PROSTORNOG PLANIRANJA I INFRASTRUKTURE
MINISTRY OF ENVIRONMENT, SPATIAL PLANNING AND INFRASTRUCTURE

AGJENCIA KADASTRALE E KOSOVËS/ KATASTARSKA AGENCIJA KOSOVA/ KOSOVA CADASTRAL AGENCY


RAPORTI I NJËSISË / IZVEŠTAJ O JEDINICI / REPORT ON UNIT

Zyra Kadastrale Komunale / Opštinska Katastarska Kancelarija/ Municipal Cadastral Office: FERIZAJ

Zona Kadastrale / Katastarska Zona/ Cadastral Zone: Greme

Tipi i njësisë / Vrsta jedinice / Unit type: Parcelë / Parcela / Parcel

Numri i njësisë kadastrale / Broj katastarske jedinice / Cadastre unit number - P-72217024-00983-0

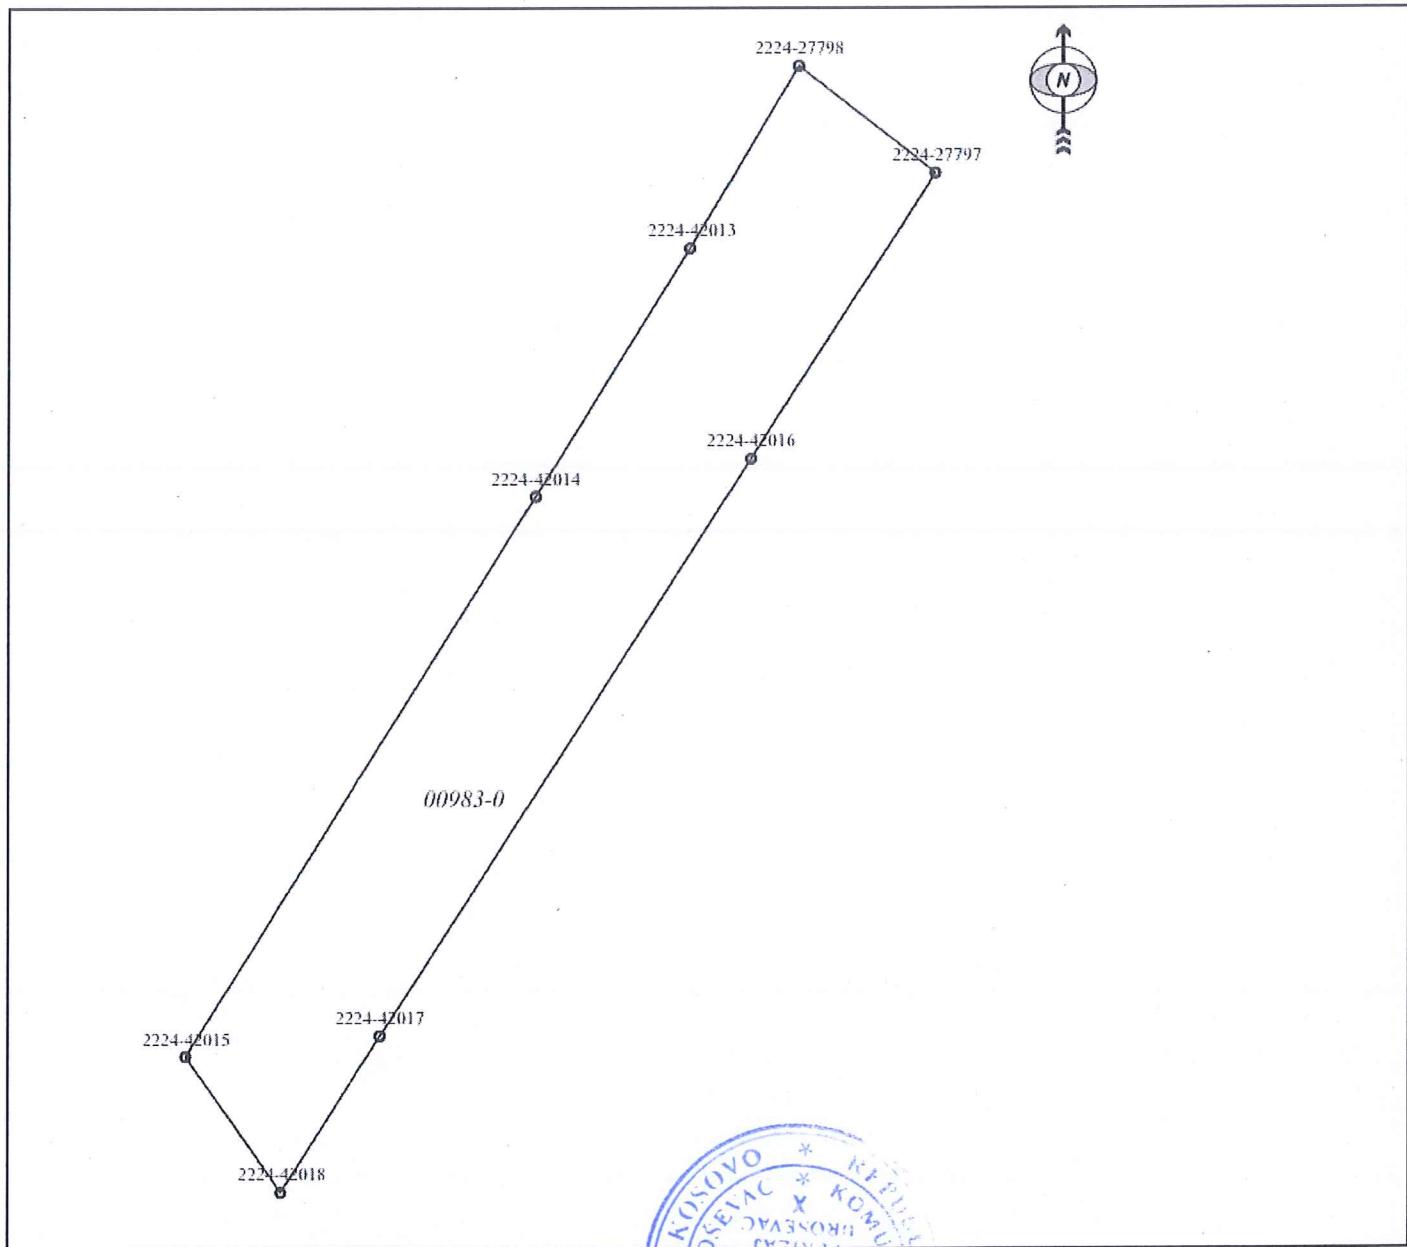

Punoi / Obradio / Created: Faton.Bislimi

Nënshkrimi / Potpis / Signature:



Data/ Data/Date: 26.08.2025

Koha/ Vreme/ Time: 09:04:42



REPUBLIKA E KOSOVËS / REPUBLIKA KOSOVA / REPUBLIC OF KOSOVO

QEVERIA E KOSOVËS / VLADA KOSOVA / GOVERNMENT OF KOSOVA

MINISTRIA E MJEDISIT, PLANIFIKIMIT HAPËSINOR DHE INFRASTRUKTURËS
MINISTARSTVO ŽIVOTNE SREDINE, PROSTORNOG PLANIRANJA I INFRASTRUKTURE
MINISTRY OF ENVIRONMENT, SPATIAL PLANNING AND INFRASTRUCTURE

AGJENCIA KADASTRALE E KOSOVËS/ KATASTARSKA AGENCIJA KOSOVA/ KOSOVA CADASTRAL AGENCY

RAPORTI I NJËSISË / IZVEŠTAJ O JEDINICI / REPORT ON UNIT

Shkalla/Razmëra/Scale: 1:1008

No	Pika / Tačka / Point	Y	X
1	2224-27797	7515650.813	4686741.508
2	2224-27798	7515635.923	4686753.259
3	2224-42013	7515624.022	4686733.240
4	2224-42014	7515607.061	4686705.972
5	2224-42015	7515568.669	4686644.516
6	2224-42016	7515630.742	4686710.091
7	2224-42017	7515590.089	4686646.755
8	2224-42018	7515579.219	4686629.577

Sip. graf. 2298m²

Proceset paraprake / Prethodni procesi / Preview processes

Rasti / Slučaj / Case	ID e procesit / ID procesa / Process ID	Datë / Datum / Date
1	597	29.04.2014.

Punoi / Obradio / Created: Faton.Bislimi

Nënshkrimi / Potpis / Signature:



Data/ Data/Date: 26.08.2025

Koha/ Vreme/ Time: 09:04:42



REPUBLIKA E KOSOVËS / REPUBLIKA KOSOVA / REPUBLIC OF KOSOVO

QEVERIA E KOSOVËS / VLADA KOSOVA / GOVERNMENT OF KOSOVA

MINISTRIA E MJEDISIT, PLANIFIKIMIT HAPËSINOR DHE INFRASTRUKTURËS
MINISTARSTVO ŽIVOTNE SREDINE, PROSTORNOG PLANIRANJA I INFRASTRUKTURE
MINISTRY OF ENVIRONMENT, SPATIAL PLANNING AND INFRASTRUCTURE

AGJENCIA KADASTRALE E KOSOVËS/ KATASTARSKA AGENCIJA KOSOVA/ KOSOVA CADASTRAL AGENCY


RAPORTI I NJËSISË / IZVEŠTAJ O JEDINICI / REPORT ON UNIT

Zyra Kadastrale Komunale / Opštinska Katastarska Kancelarija/ Municipal Cadastral Office: **FERIZAJ**

Zona Kadastrale / Katastarska Zona/ Cadastral Zone: **Greme**

Tipi i njësisë / Vrsta jedinice / Unit type: **Parcelë / Parcela / Parcel**

Numri i njësisë kadastrale / Broj katastarske jedinice / Cadastre unit number - **P-72217024-00984-0**

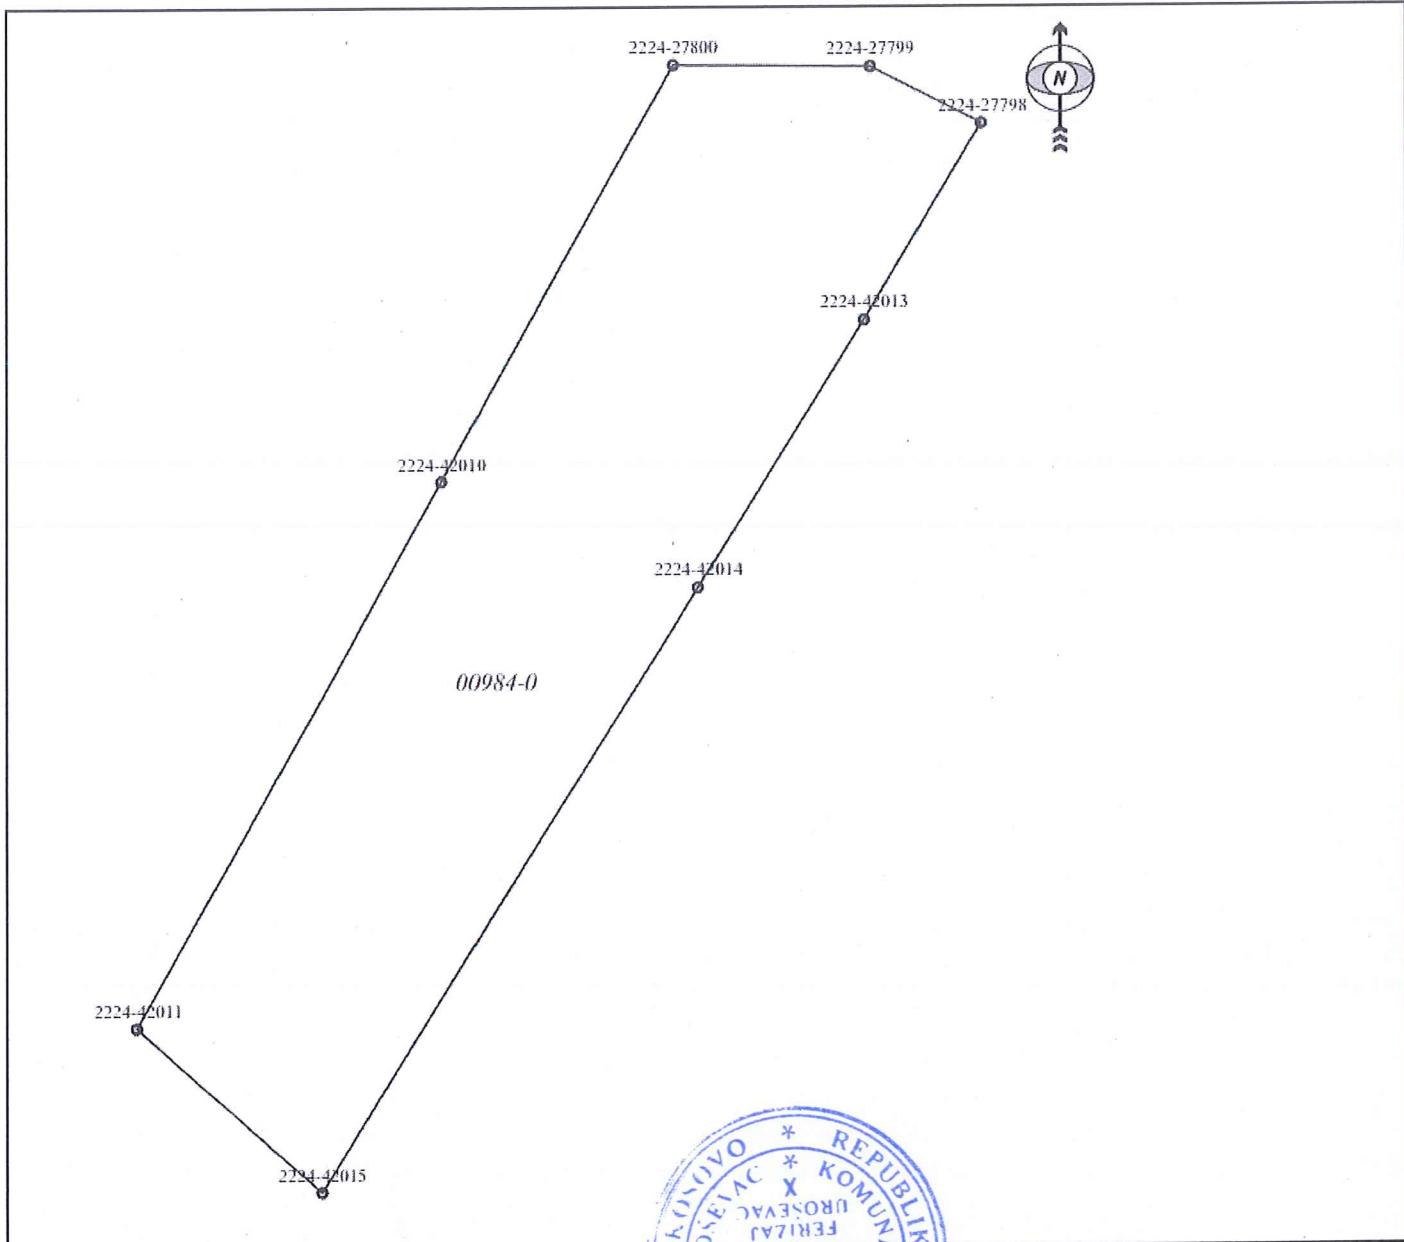

Punoi / Obradio / Created: Faton.Bislimi

Nënshkrimi / Potpis / Signature:

Data/ Data/Date: 26.08.2025

Koha/ Vreme/ Time: 09:05:33





REPUBLIKA E KOSOVËS / REPUBLIKA KOSOVA / REPUBLIC OF KOSOVO

QEVERIA E KOSOVËS / VLADA KOSOVA / GOVERNMENT OF KOSOVA

MINISTRIA E MJEDISIT, PLANIFIKIMIT HAPËSINOR DHE INFRASTRUKTURËS
MINISTARSTVO ŽIVOTNE SREDINE, PROSTORNOG PLANIRANJA I INFRASTRUKTURE
MINISTRY OF ENVIRONMENT, SPATIAL PLANNING AND INFRASTRUCTURE

AGJENCIA KADASTRALE E KOSOVËS/ KATASTARSKA AGENCIJA KOSOVA/ KOSOVA CADASTRAL AGENCY

RAPORTI I NJËSISË / IZVEŠTAJ O JEDINICI / REPORT ON UNIT

Shkalla/Razmëra/Scale: 1:935

No	Pika / Tačka / Point	Y	X
1	2224-27798	7515635.923	4686753.259
2	2224-27799	7515624.683	4686759.089
3	2224-27800	7515604.513	4686759.300
4	2224-42010	7515580.982	4686716.842
5	2224-42011	7515549.860	4686661.306
6	2224-42013	7515624.022	4686733.240
7	2224-42014	7515607.061	4686705.972
8	2224-42015	7515568.669	4686644.516

si p qef. 3370 m²

Proceset paraprake / Prethodni procesi / Preview processes

Rasti / Slučaj / Case	ID e procesit / ID procesa / Process ID	Datë / Datum / Date
1	597	29.04.2014.

Punoi / Obradio / Created: Faton.Bislimi

Nënshkrimi / Potpis / Signature: _____

Data/ Data/Date: 26.08.2025

Koha/ Vreme/ Time: 09:05:33





REPUBLIKA E KOSOVËS / REPUBLIKA KOSOVA / REPUBLIC OF KOSOVO

QEVERTA E KOSOVËS / VLADA KOSOVA / GOVERNMENT OF KOSOVA

MINISTRIA E MJEDISIT, PLANIFIKIMIT HAPËSINOR DHE INFRASTRUKTURËS
MINISTARSTVO ŽIVOTNE SREDINE, PROSTORNOG PLANIRANJA I INFRASTRUKTURE
MINISTRY OF ENVIRONMENT, SPATIAL PLANNING AND INFRASTRUCTURE

AGJENCIA KADASTRALE E KOSOVËS/ KATASTARSKA AGENCIJA KOSOVA/ KOSOVA CADASTRAL AGENCY


RAPORTI I NJËSISË / IZVEŠTAJ O JEDINICI / REPORT ON UNIT

Zyra Kadastrale Komunale / Opštinska Katastarska Kancelarija/ Municipal Cadastral Office: **FERIZAJ**

Zona Kadastrale / Katastarska Zona/ Cadastral Zone: **Greme**

Tipi i njësisë / Vrsta jedinice / Unit type: **Parcelë / Parcela / Parcel**

Numri i njësisë kadastrale / Broj katastarske jedinice / Cadastre unit number - **P-72217024-01024-0**

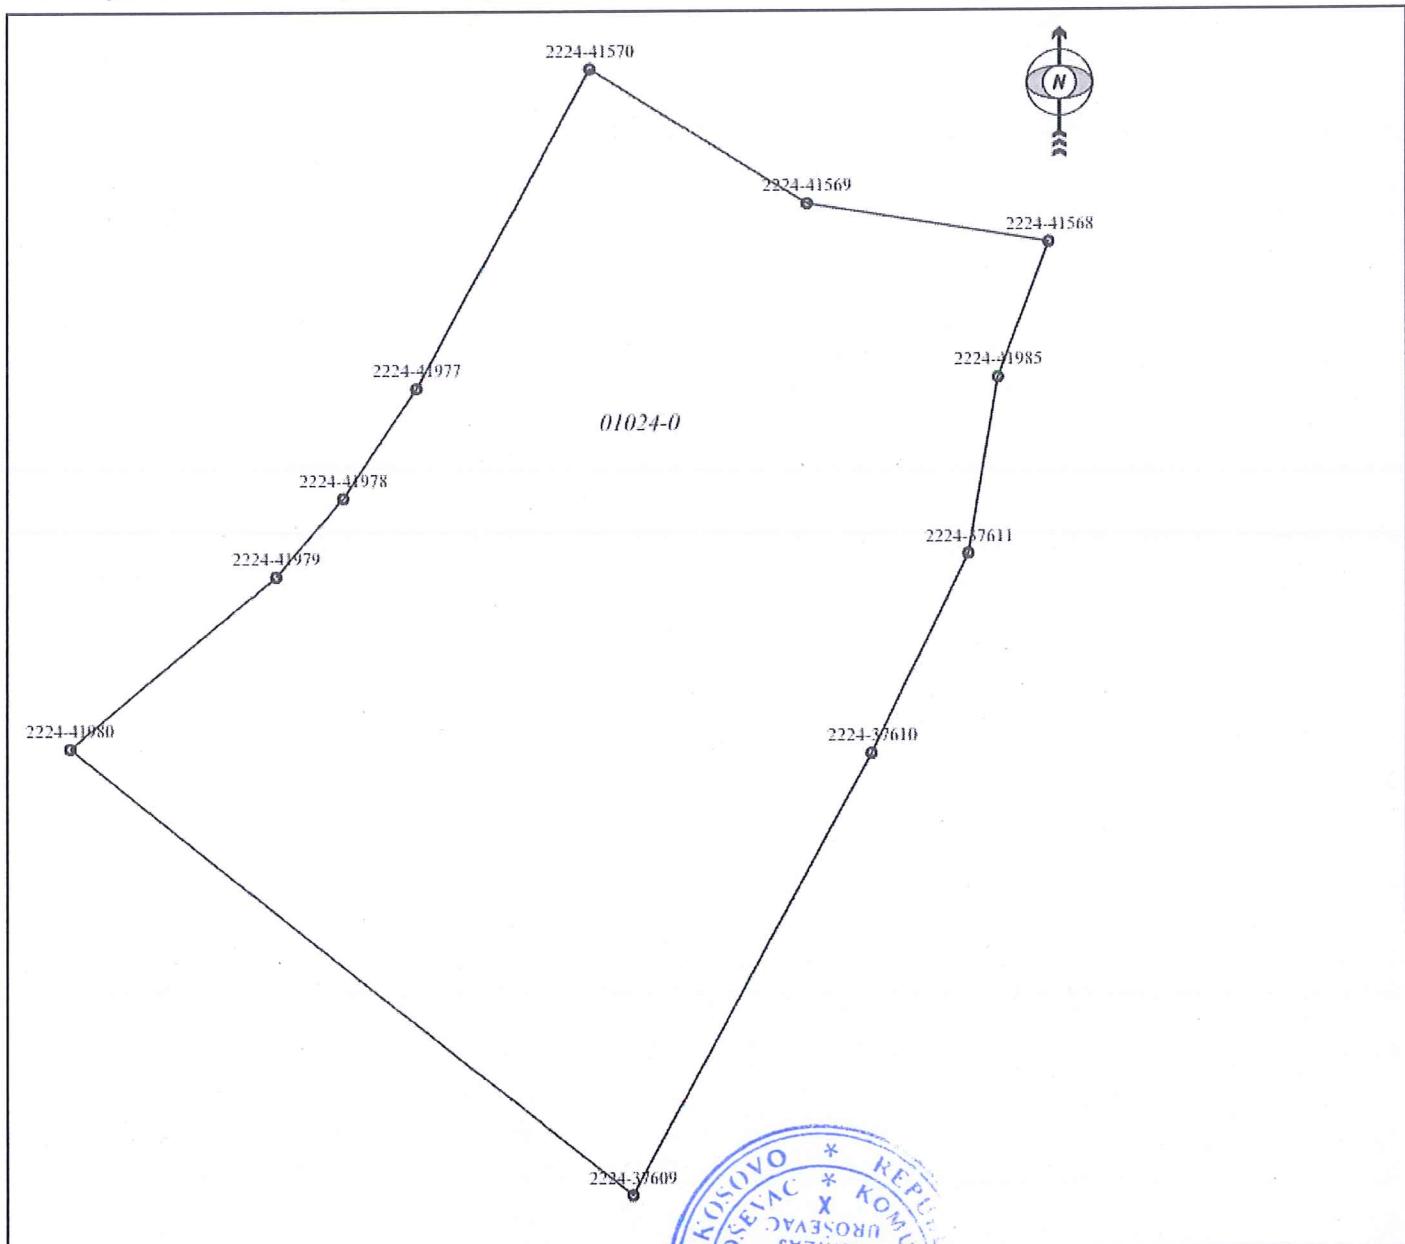

Punoi / Obradio / Created: Faton.Bislimi

Nënshkrimi / Potpis / Signature:

Data/ Data/Date: 26.08.2025

Koha/ Vreme/ Time: 09:06:37



REPUBLIKA E KOSOVËS / REPUBLIKA KOSOVA / REPUBLIC OF KOSOVO

QEVERIA E KOSOVËS / VLADA KOSOVA / GOVERNMENT OF KOSOVA

MINISTRIA E MJEDISIT, PLANIFIKIMIT HAPËSINOR DHE INFRASTRUKTURËS
MINISTARSTVO ŽIVOTNE SREDINE, PROSTORNOG PLANIRANJA I INFRASTRUKTURE
MINISTRY OF ENVIRONMENT, SPATIAL PLANNING AND INFRASTRUCTURE

AGJENCIA KADASTRALE E KOSOVËS/ KATASTARSKA AGENCIJA KOSOVA/ KOSOVA CADASTRAL AGENCY

RAPORTI I NJËSISË / IZVEŠTAJ O JEDINICI / REPORT ON UNIT

Shkalla/Razmëra/Scale: 1:988

No	Pika / Tačka / Point	Y	X
1	2224-37609	7515364.497	4686583.558
2	2224-37610	7515390.068	4686631.034
3	2224-37611	7515400.439	4686652.573
4	2224-41568	7515409.140	4686686.121
5	2224-41569	7515383.230	4686690.322
6	2224-41570	7515359.831	4686704.872
7	2224-41977	7515341.190	4686670.545
8	2224-41978	7515333.329	4686658.755
9	2224-41979	7515326.069	4686650.306
10	2224-41980	7515303.718	4686631.878
11	2224-41985	7515403.640	4686671.542

sip prof. 6301.6~

Proceset paraprake / Prethodni procesi / Preview processes

Rasti / Slučaj / Case	ID e procesit / ID procesa / Process ID	Datë / Datum / Date
1	597	29.04.2014.

Punoi / Obradio / Created: Faton.Bislimi

Nënshkrimi / Potpis / Signature: _____

Data/ Data/Date: 26.08.2025

Koha/ Vreme/ Time: 09:06:37





REPUBLIKA E KOSOVËS / REPUBLIKA KOSOVA / REPUBLIC OF KOSOVO

QEVERIA E KOSOVËS / VLADA KOSOVA / GOVERNMENT OF KOSOVA

MINISTRIA E MJEDISIT, PLANIFIKIMIT HAPËSINOR DHE INFRASTRUKTURËS
MINISTARSTVO ŽIVOTNE SREDINE, PROSTORNOG PLANIRANJA I INFRASTRUKTURE
MINISTRY OF ENVIRONMENT, SPATIAL PLANNING AND INFRASTRUCTURE

AGJENCIA KADASTRALE E KOSOVËS/ KATASTARSKA AGENCIJA KOSOVA/ KOSOVA CADASTRAL AGENCY


RAPORTI I NJËSISË / IZVEŠTAJ O JEDINICI / REPORT ON UNIT

Zyra Kadastrale Komunale / Opštinska Katastarska Kancelarija/ Municipal Cadastral Office: FERIZAJ

Zona Kadastrale / Katastarska Zona/ Cadastral Zone: Greme

Tipi i njësisë / Vrsta jedinice / Unit type: Parcelë / Parcela / Parcel

Numri i njësisë kadastrale / Broj katastarske jedinice / Cadastre unit number - P-72217024-01703-1

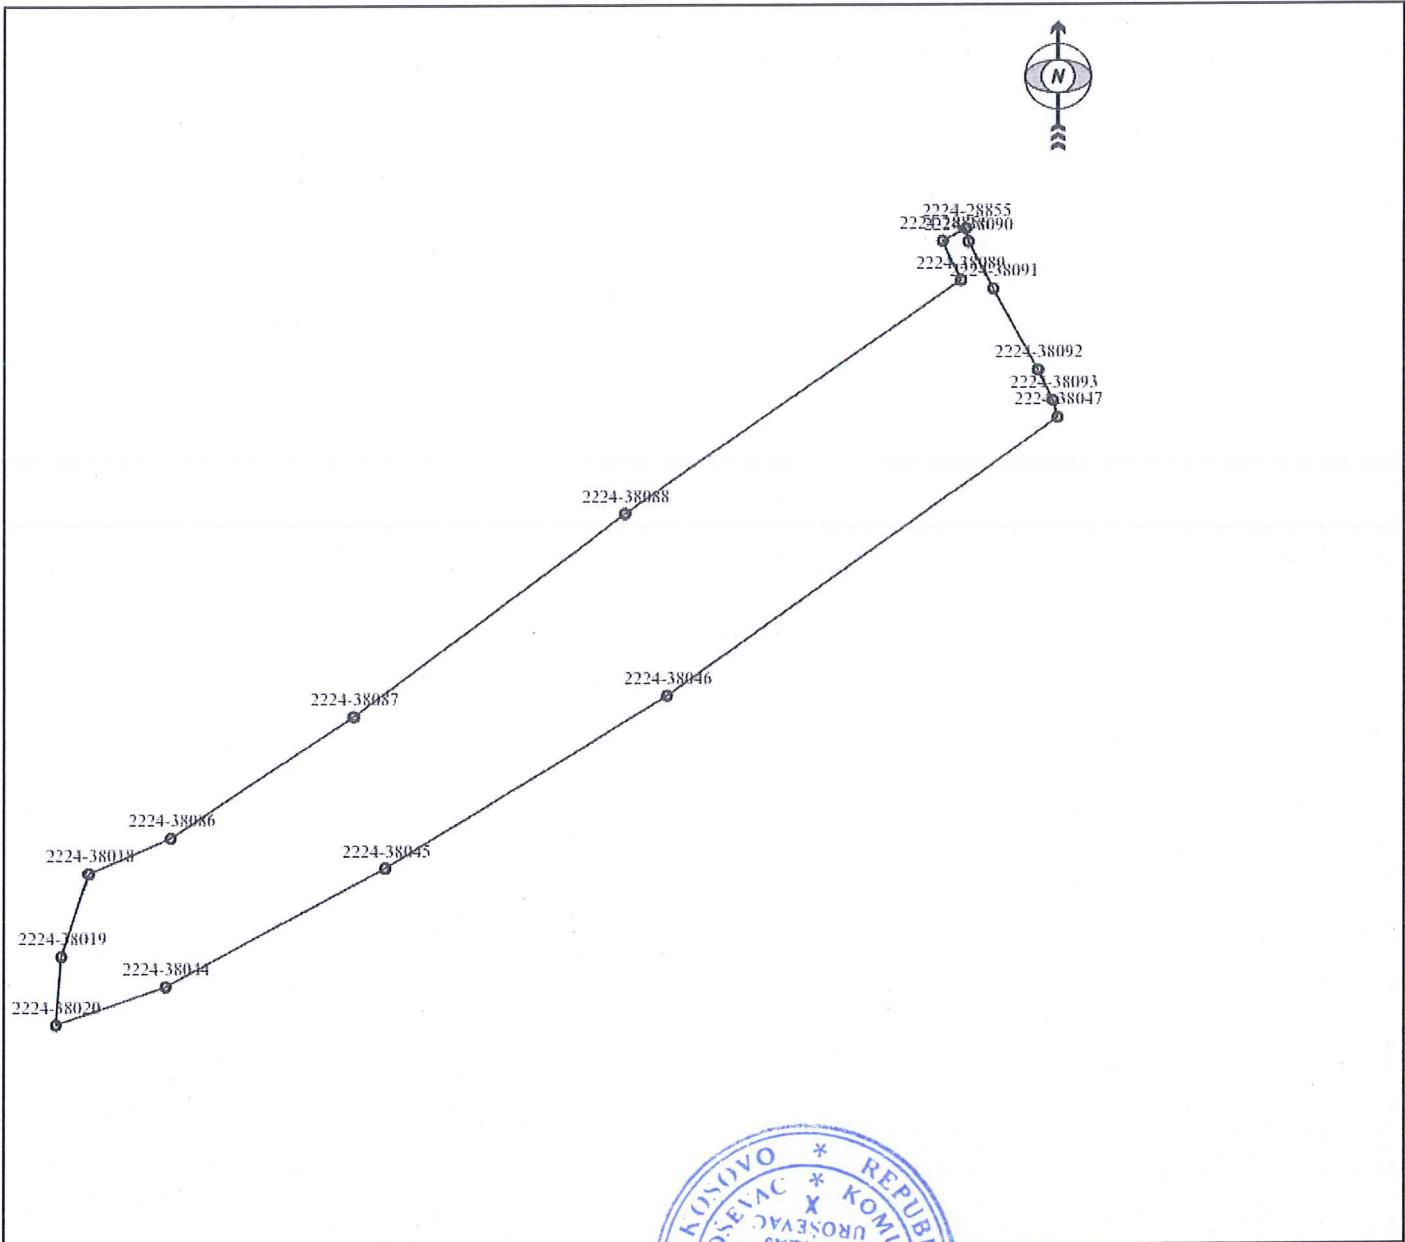

Puni / Obradio / Created: Faton.Bislimi

Nënshkrimi / Potpis / Signature:

Data/ Data/Date: 26.08.2025

Koha/ Vreme/ Time: 09:07:58





REPUBLIKA E KOSOVËS / REPUBLIKA KOSOVA / REPUBLIC OF KOSOVO

QEVERIA E KOSOVËS / VLADA KOSOVA / GOVERNMENT OF KOSOVA

MINISTRIA E MJEDISIT, PLANIFIKIMIT HAPËSINOR DHE INFRASTRUKTURËS
MINISTARSTVO ŽIVOTNE SREDINE, PROSTORNOG PLANIRANJA I INFRASTRUKTURE
MINISTRY OF ENVIRONMENT, SPATIAL PLANNING AND INFRASTRUCTURE

AGJENCIA KADASTRALE E KOSOVËS/ KATASTARSKA AGENCIJA KOSOVA/ KOSOVA CADASTRAL AGENCY

RAPORTI I NJËSISË / IZVEŠTAJ O JEDINICI / REPORT ON UNIT

Shkalla/Razmera/Scale: 1:1367

No	Pika / Tačka / Point	Y	X
1	2224-28855	7514543.080	4686497.150
2	2224-28856	7514539.752	4686495.296
3	2224-38018	7514412.548	4686401.395
4	2224-38019	7514408.478	4686389.126
5	2224-38020	7514407.638	4686378.977
6	2224-38044	7514424.058	4686384.576
7	2224-38045	7514456.928	4686402.034
8	2224-38046	7514498.919	4686427.681
9	2224-38047	7514556.780	4686469.030
10	2224-38086	7514424.829	4686406.625
11	2224-38087	7514452.249	4686424.693
12	2224-38088	7514492.630	4686454.820
13	2224-38089	7514542.372	4686489.456
14	2224-38090	7514543.460	4686495.180
15	2224-38091	7514547.130	4686488.190
16	2224-38092	7514553.860	4686476.110
17	2224-38093	7514556.110	4686471.550

sig. prof. 3959, f-

Proceset paraprake / Prethodni procesi / Preview processes

Rasti / Slučaj / Case	ID e procesit / ID procesa / Process ID	Datë / Datum / Date
65437/25KP	716874	22.08.2025.
1	597	29.04.2014.

Puni / Obradio / Created: Faton.Bislimi

Nënshkrimi / Potpis / Signature:



Data/ Data/Date: 26.08.2025

Koha/ Vreme/ Time: 09:07:58



REPUBLIKA E KOSOVËS / REPUBLIKA KOSOVA / REPUBLIC OF KOSOVO

QEVERIA E KOSOVËS / VLADA KOSOVA / GOVERNMENT OF KOSOVA

MINISTRIA E MJEDISIT, PLANIFIKIMIT HAPËSINOR DHE INFRASTRUKTURËS
MINISTARSTVO ŽIVOTNE SREDINE, PROSTORNOG PLANIRANJA I INFRASTRUKTURE
MINISTRY OF ENVIRONMENT, SPATIAL PLANNING AND INFRASTRUCTURE

AGJENCIA KADASTRALE E KOSOVËS/ KATASTARSKA AGENCIJA KOSOVA/ KOSOVA CADASTRAL AGENCY


RAPORTI I NJËSISË / IZVEŠTAJ O JEDINICI / REPORT ON UNIT

Zyra Kadastrale Komunale / Opštinska Katastarska Kancelarija/ Municipal Cadastral Office: **FERIZAJ**

Zona Kadastrale / Katastarska Zona/ Cadastral Zone: **Greme**

Tipi i njësisë / Vrsta jedinice / Unit type: **Parcelë / Parcela / Parcel**

Numri i njësisë kadastrale / Broj katastarske jedinice / Cadastre unit number - **P-72217024-01706-0**

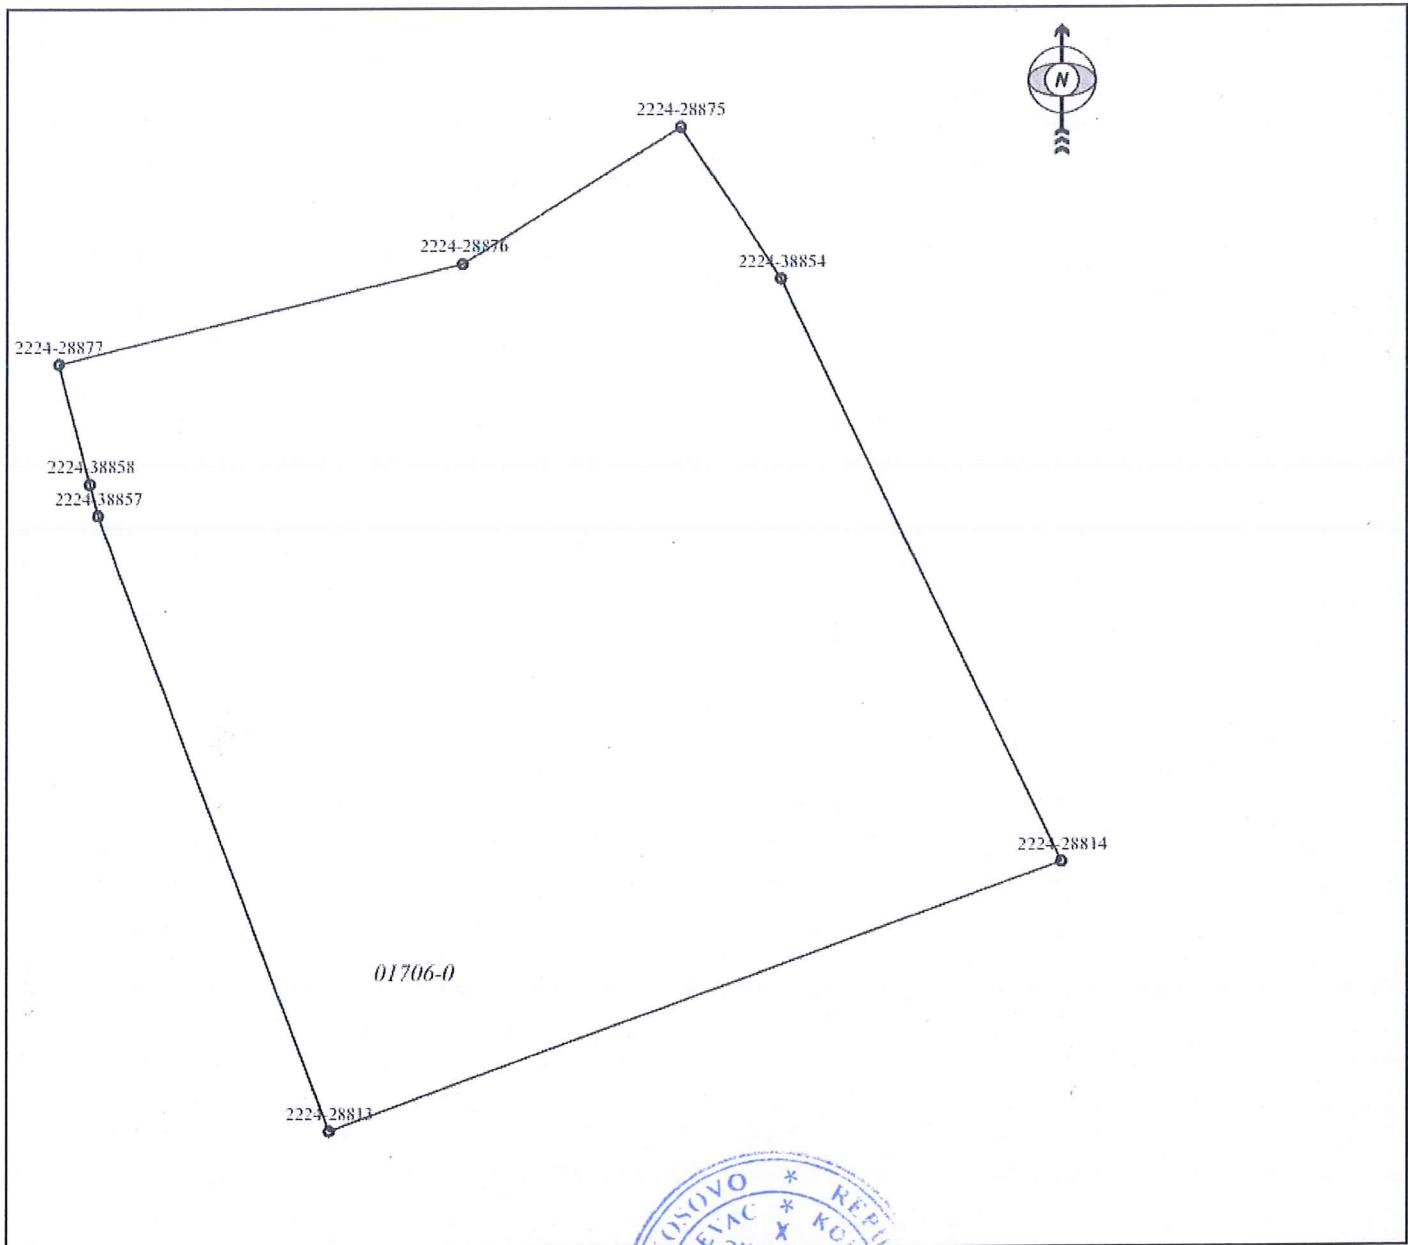

Puni / Obradio / Created: Faton.Bislimi

Nënshkrimi / Potpis / Signature:

Data/ Data/Date: 26.08.2025

Koha/ Vreme/ Time: 09:09:53



REPUBLIKA E KOSOVËS / REPUBLIKA KOSOVA / REPUBLIC OF KOSOVO

QEVERIA E KOSOVËS / VLADA KOSOVA / GOVERNMENT OF KOSOVA

MINISTRIA E MJEDISIT, PLANIFIKIMT HAPËSINOR DHE INFRASTRUKTURËS
MINISTARSTVO ŽIVOTNE SREDINE, PROSTORNOG PLANIRANJA I INFRASTRUKTURE
MINISTRY OF ENVIRONMENT, SPATIAL PLANNING AND INFRASTRUCTURE

AGJENCIA KADASTRALE E KOSOVËS/ KATASTARSKA AGENCIJA KOSOVA/ KOSOVA CADASTRAL AGENCY

RAPORTI I NJËSISË / IZVEŠTAJ O JEDINICI / REPORT ON UNIT

Shkalla/Razmera/Scale: 1:305

No	Pika / Tačka / Point	Y	X
1	2224-28813	7514505.722	4686494.467
2	2224-28814	7514530.022	4686503.376
3	2224-28875	7514517.393	4686527.855
4	2224-28876	7514510.193	4686523.306
5	2224-28877	7514496.743	4686519.987
6	2224-38854	7514520.723	4686522.785
7	2224-38857	7514498.063	4686514.967
8	2224-38858	7514497.790	4686516.010

597-6483-22

Proceset paraprake / Prethodni procesi / Preview processes

Rasti / Slučaj / Case	ID e procesit / ID procesa / Process ID	Datë / Datum / Date
1	597	29.04.2014.

Punoi / Obradio / Created: Faton.Bislimi

Nënshkrimi / Potpis / Signature:

Data/ Data/Date: 26.08.2025

Koha/ Vreme/ Time: 09:09:53





REPUBLIKA E KOSOVËS / REPUBLIKA KOSOVA / REPUBLIC OF KOSOVO

QEVERIA E KOSOVËS / VLADA KOSOVA / GOVERNMENT OF KOSOVO

MINISTRIA E MJEDISIT, PLANIFIKIMIT HAPËSINOR DHE INFRASTRUKTURËS
MINISTARSTVO ŽIVOTNE SREDINE, PROSTORNOG PLANIRANJA I INFRASTRUKTURE
MINISTRY OF ENVIRONMENT, SPATIAL PLANNING AND INFRASTRUCTURE

AGJENCIA KADASTRALE E KOSOVËS/ KATASTARSKA AGENCIJA KOSOVA/ KOSOVA CADASTRAL AGENCY


RAPORTI I NJËSISË / IZVEŠTAJ O JEDINICI / REPORT ON UNIT

Zyra Kadastrale Komunale / Opštinska Katastarska Kancelarija/ Municipal Cadastral Office: **FERIZAJ**

Zona Kadastrale / Katastarska Zona/ Cadastral Zone: **Greme**

Tipi i njësisë / Vrsta jedinice / Unit type: **Parcelë / Parcela / Parcel**

Numri i njësisë kadastrale / Broj katastarske jedinice / Cadastre unit number - **P-72217024-01707-0**

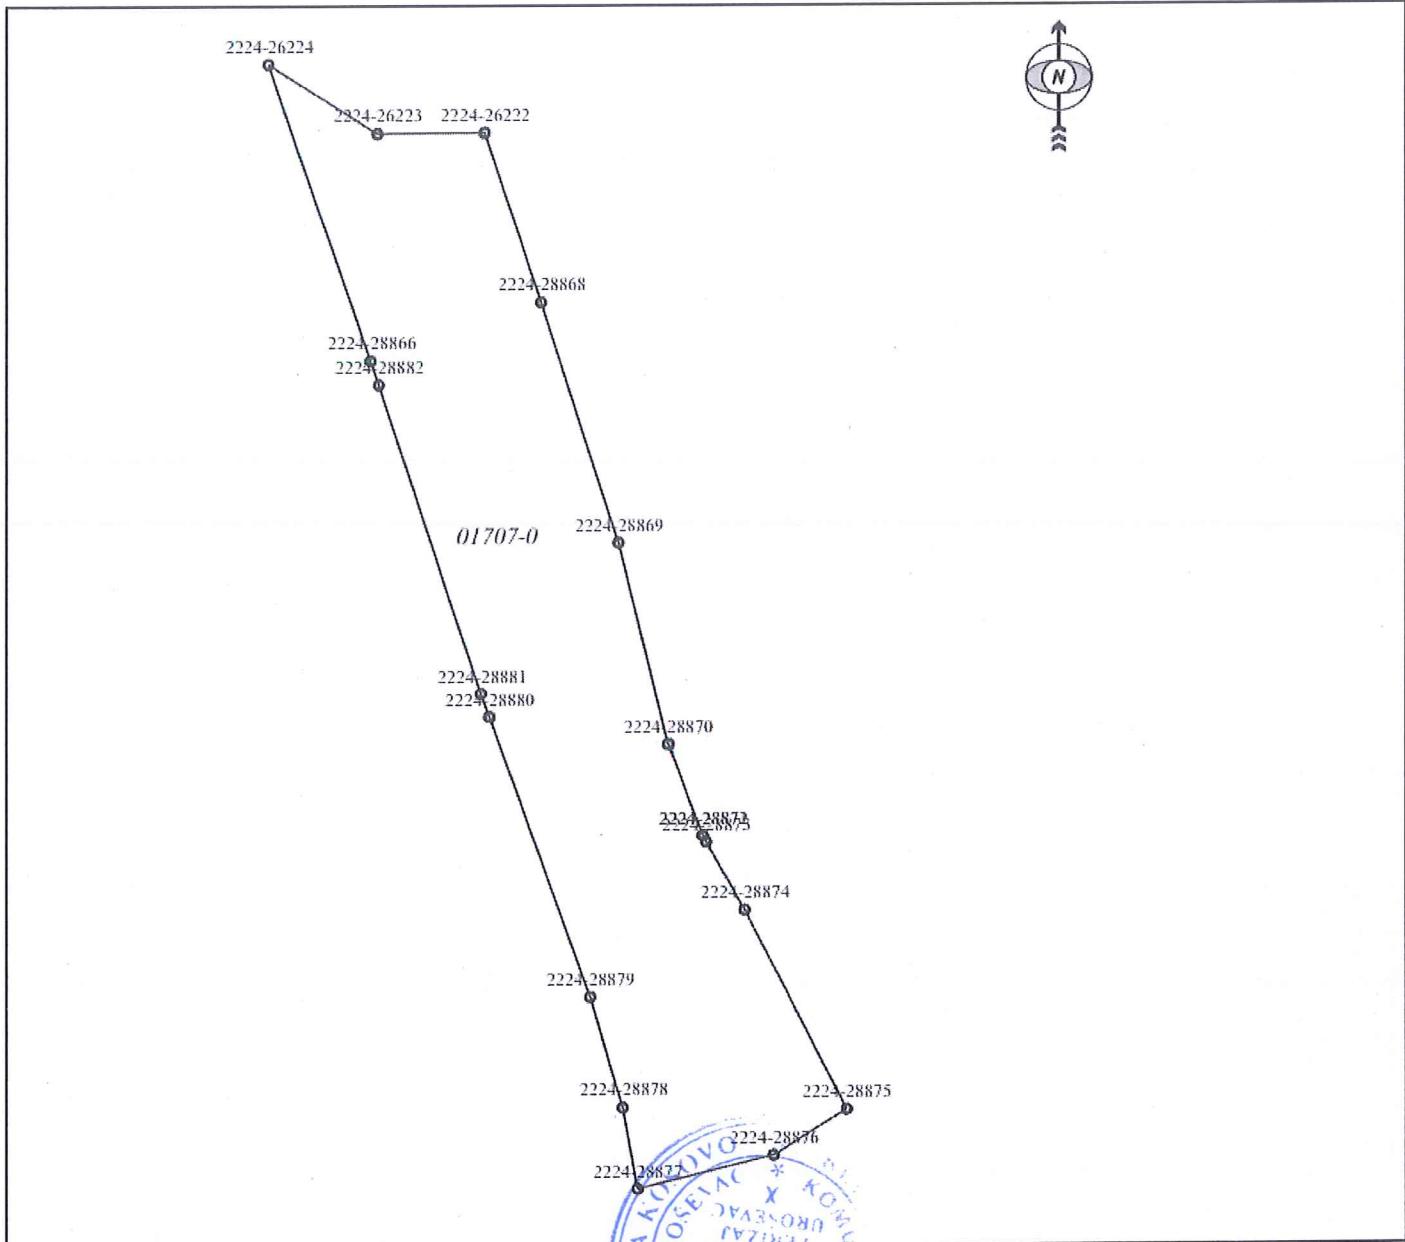

Punoi / Obradio / Created: Faton.Bislimi

Nënshkrimi / Potpis / Signature:



Data/ Data/Date: 26.08.2025

Koha/ Vreme/ Time: 09:43:29



REPUBLIKA E KOSOVËS / REPUBLIKA KOSOVA / REPUBLIC OF KOSOVO

QEVERIA E KOSOVËS / VLADA KOSOVA / GOVERNMENT OF KOSOVA

MINISTRIA E MJEDISIT, PLANIFIKIMIT HAPËSINOR DHE INFRASTRUKTURËS
MINISTARSTVO ŽIVOTNE SREDINE, PROSTORNOG PLANIRANJA I INFRASTRUKTURE
MINISTRY OF ENVIRONMENT, SPATIAL PLANNING AND INFRASTRUCTURE

AGJENCIA KADASTRALE E KOSOVËS/ KATASTARSKA AGENCIJA KOSOVA/ KOSOVA CADASTRAL AGENCY

RAPORTI I NJËSISË / IZVEŠTAJ O JEDINICI / REPORT ON UNIT

Shkalla/Razmera/Scale: 1:913

No	Pika / Tačka / Point	Y	X
1	2224-26222	7514481.417	4686625.242
2	2224-26223	7514470.817	4686625.163
3	2224-26224	7514459.967	4686632.063
4	2224-28866	7514470.150	4686602.509
5	2224-28868	7514487.046	4686608.283
6	2224-28869	7514494.825	4686584.344
7	2224-28870	7514499.774	4686564.254
8	2224-28871	7514503.184	4686555.155
9	2224-28872	7514503.184	4686555.145
10	2224-28873	7514503.524	4686554.545
11	2224-28874	7514507.354	4686547.755
12	2224-28875	7514517.393	4686527.855
13	2224-28876	7514510.193	4686523.306
14	2224-28877	7514496.743	4686519.987
15	2224-28878	7514495.233	4686528.076
16	2224-28879	7514492.013	4686539.106
17	2224-28880	7514481.889	4686567.022
18	2224-28881	7514481.060	4686569.307
19	2224-28882	7514470.967	4686600.137

St.p.graf. 1998.17nr

Proceset paraprake / Prethodni procesi / Preview processes

Rasti / Slučaj / Case	ID e procesit / ID procesa / Process ID	Datë / Datum / Date
1	597	29.04.2014.

Punoi / Obradio / Created: Faton.Bislimi

Nënshkrimi / Potpis / Signature:



Data/ Data/Date: 26.08.2025

Koha/ Vreme/ Time: 09:43:29



REPUBLIKA E KOSOVËS / REPUBLIKA KOSOVA / REPUBLIC OF KOSOVO

QEVERIA E KOSOVËS / VLADA KOSOVA / GOVERNMENT OF KOSOVA

MINISTRIA E MJEDISIT, PLANIFIKIMIT HAPËSINOR DHE INFRASTRUKTURËS
MINISTARSTVO ŽIVOTNE SREDINE, PROSTORNOG PLANIRANJA I INFRASTRUKTURE
MINISTRY OF ENVIRONMENT, SPATIAL PLANNING AND INFRASTRUCTURE

AGJENCIA KADASTRALE E KOSOVËS/ KATASTARSKA AGENCIJA KOSOVA/ KOSOVA CADASTRAL AGENCY


RAPORTI I NJËSISË / IZVEŠTAJ O JEDINICI / REPORT ON UNIT

Zyra Kadastrale Komunale / Opštinska Katastarska Kancelarija/ Municipal Cadastral Office: FERIZAJ

Zona Kadastrale / Katastarska Zona/ Cadastral Zone: Greme

Tipi i njësisë / Vrsta jedinice / Unit type: Parcelë / Parcela / Parcel

Numri i njësisë kadastrale / Broj katastarske jedinice / Cadastre unit number - P-72217024-01720-0

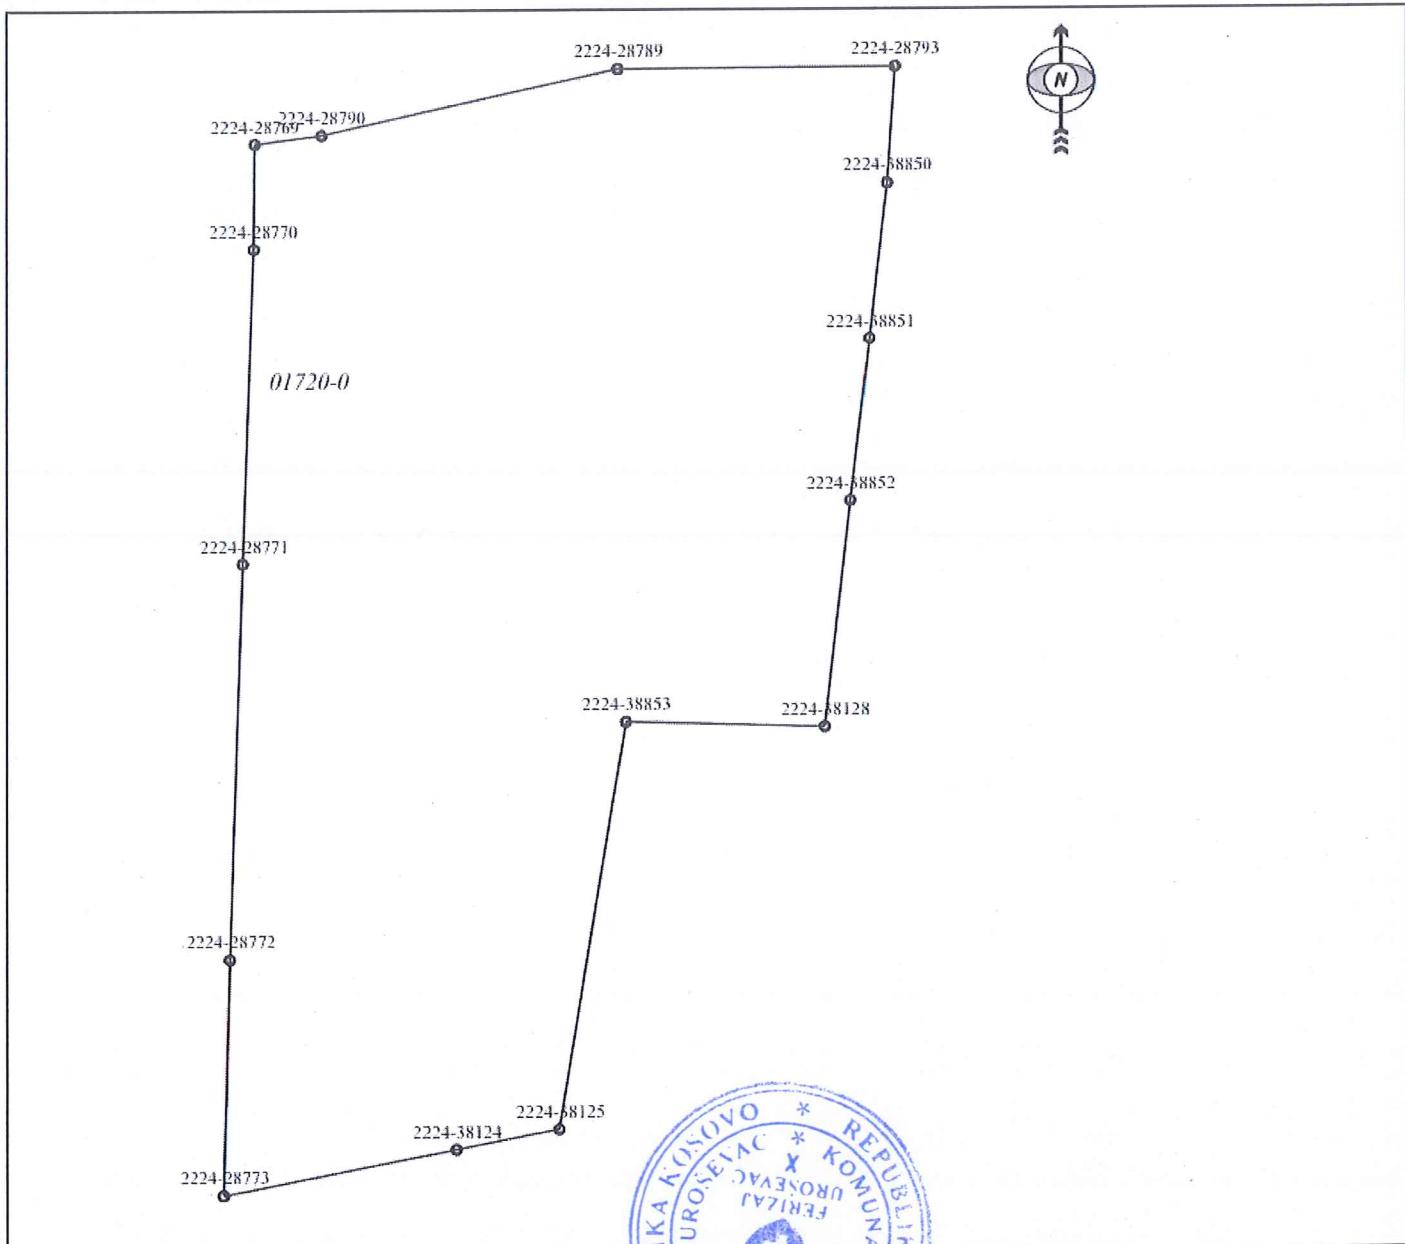

Puni / Obradio / Created: Faton.Bislimi

Nënshkrimi / Potpis / Signature:

Data/ Data/Date: 26.08.2025

Koha/ Vreme/ Time: 09:44:36





REPUBLIKA E KOSOVËS / REPUBLIKA KOSOVA / REPUBLIC OF KOSOVO

QEVERIA E KOSOVËS / VLADA KOSOVA / GOVERNMENT OF KOSOVA

MINISTRIA E MJEDISIT, PLANIFIKIMIT HAPËSINOR DHE INFRASTRUKTURËS
MINISTARSTVO ŽIVOTNE SREDINE, PROSTORNOG PLANIRANJA I INFRASTRUKTURE
MINISTRY OF ENVIRONMENT, SPATIAL PLANNING AND INFRASTRUCTURE

AGJENCIA KADASTRALE E KOSOVËS/ KATASTARSKA AGENCIJA KOSOVA/ KOSOVA CADASTRAL AGENCY

RAPORTI I NJËSISË / IZVEŠTAJ O JEDINICI / REPORT ON UNIT

Shkalla/Razmera/Scale: 1:691

No	Pika / Tačka / Point	Y	X
1	2224-28769	7514307.455	4686595.061
2	2224-28770	7514307.385	4686587.201
3	2224-28771	7514306.554	4686563.502
4	2224-28772	7514305.583	4686533.704
5	2224-28773	7514305.132	4686515.955
6	2224-28789	7514334.835	4686600.610
7	2224-28790	7514312.565	4686595.711
8	2224-28793	7514355.735	4686600.729
9	2224-38124	7514322.762	4686519.364
10	2224-38125	7514330.443	4686520.853
11	2224-38128	7514350.464	4686551.041
12	2224-38850	7514355.145	4686591.969
13	2224-38851	7514353.815	4686580.320
14	2224-38852	7514352.394	4686568.100
15	2224-38853	7514335.444	4686551.462

sig. 3096.6~

Proceset paraprake / Prethodni procesi / Preview processes

Rasti / Slučaj / Case	ID e procesit / ID procesa / Process ID	Datë / Datum / Date
1	597	29.04.2014.

Punoi / Obradio / Created: Faton.Bislimi

Nënshkrimi / Potpis / Signature:

Data/ Data/Date: 26.08.2025

Koha/ Vreme/ Time: 09:44:36





REPUBLIKA E KOSOVËS / REPUBLIKA KOSOVA / REPUBLIC OF KOSOVO

QEVERIA E KOSOVËS / VLADA KOSOVA / GOVERNMENT OF KOSOVA

MINISTRIA E MJEDISIT, PLANIFIKIMIT HAPËSINOR DHE INFRASTRUKTURËS
MINISTARSTVO ŽIVOTNE SREDINE, PROSTORNOG PLANIRANJA I INFRASTRUKTURE
MINISTRY OF ENVIRONMENT, SPATIAL PLANNING AND INFRASTRUCTURE

AGJENCIA KADASTRALE E KOSOVËS/ KATASTARSKA AGENCIJA KOSOVA/ KOSOVA CADASTRAL AGENCY


RAPORTI I NJËSISË / IZVEŠTAJ O JEDINICI / REPORT ON UNIT

Zyra Kadastrale Komunale / Opštinska Katastarska Kancelarija/ Municipal Cadastral Office: FERIZAJ

Zona Kadastrale / Katastarska Zona/ Cadastral Zone: Greme

Tipi i njësisë / Vrsta jedinice / Unit type: Parcelë / Parcela / Parcel

Numri i njësisë kadastrale / Broj katastarske jedinice / Cadastre unit number - P-72217024-01721-0

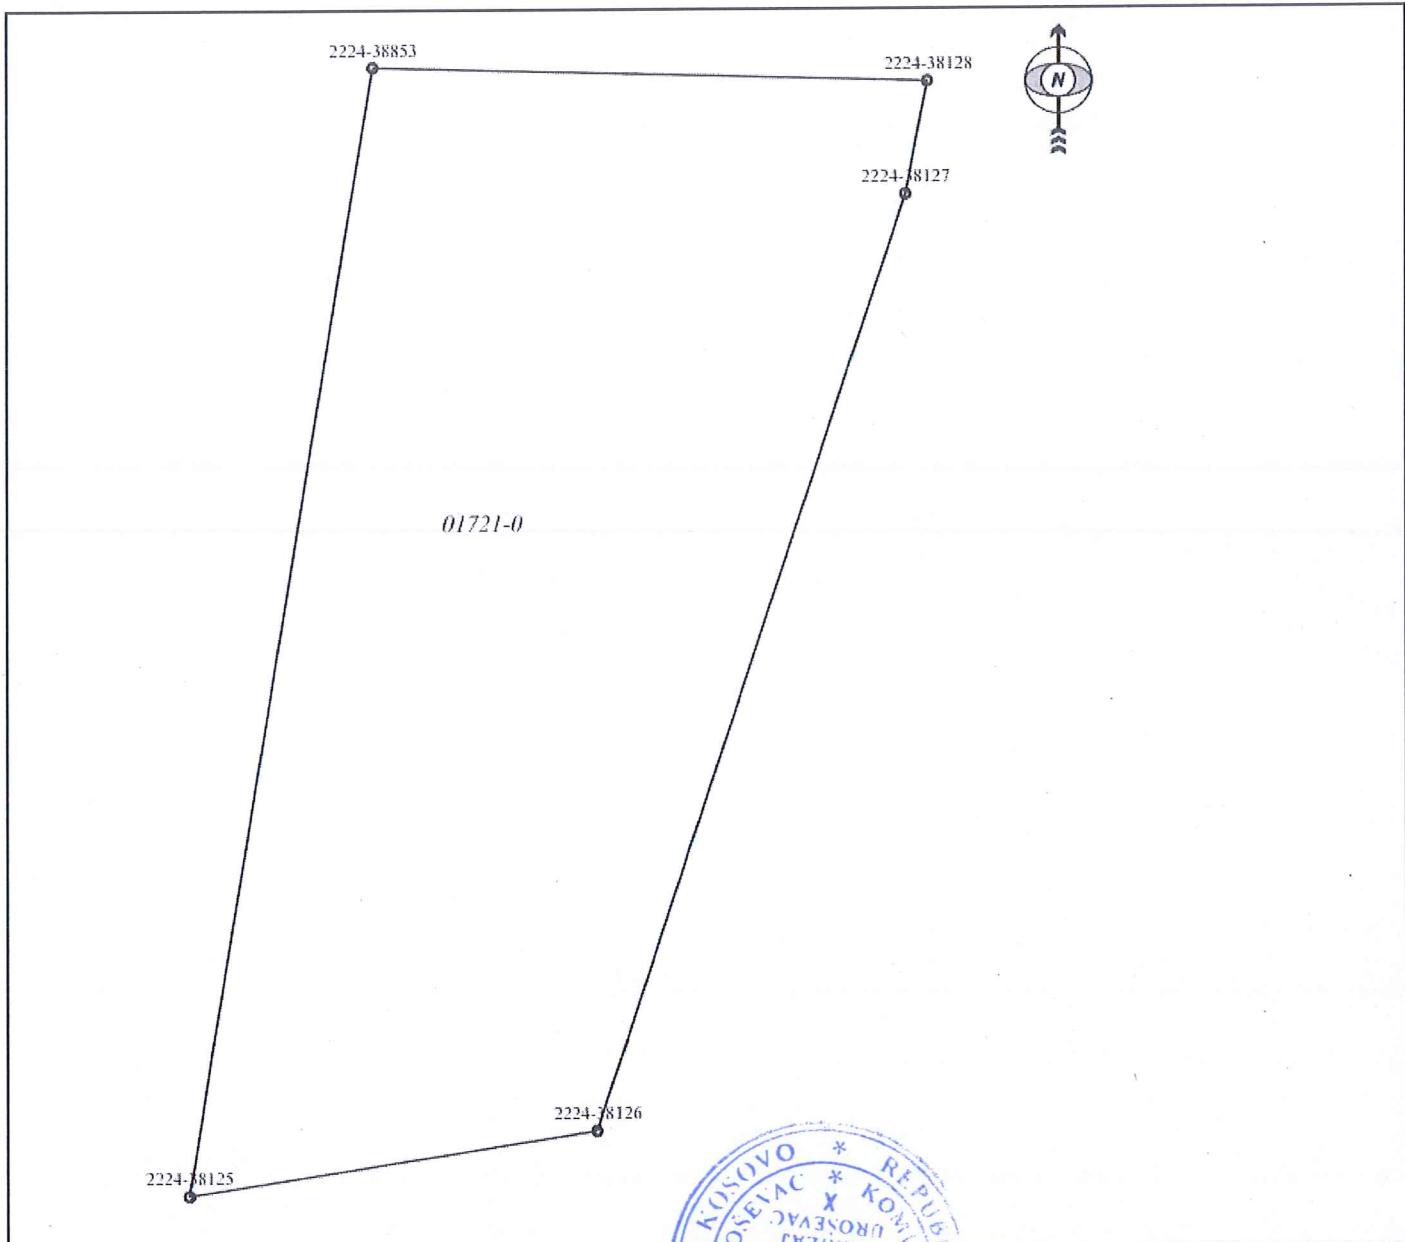

Punoi / Obradio / Created: Faton.Bislimi

Nënshkrimi / Potpis / Signature:



Data/ Data/Date: 26.08.2025

Koha/ Vreme/ Time: 09:45:21



REPUBLIKA E KOSOVËS / REPUBLIKA KOSOVA / REPUBLIC OF KOSOVO

QEVERIA E KOSOVËS / VLADA KOSOVA / GOVERNMENT OF KOSOVA

MINISTRIA E MJEDISIT, PLANIFIKIMIT HAPËSINOR DHE INFRASTRUKTURËS
MINISTARSTVO ŽIVOTNE SREDINE, PROSTORNOG PLANIRANJA I INFRASTRUKTURE
MINISTRY OF ENVIRONMENT, SPATIAL PLANNING AND INFRASTRUCTURE

AGJENCIA KADASTRALE E KOSOVËS/ KATASTARSKA AGENCIJA KOSOVA/ KOSOVA CADASTRAL AGENCY

RAPORTI I NJËSISË / IZVEŠTAJ O JEDINICI / REPORT ON UNIT

Shkalla/Razmëra/Scale: 1:249

No	Pika / Tačka / Point	Y	X
1	2224-38125	7514330.443	4686520.853
2	2224-38126	7514341.523	4686522.563
3	2224-38127	7514349.864	4686547.961
4	2224-38128	7514350.464	4686551.041
5	2224-38853	7514335.444	4686551.462

Sip gjyq. 386.3 n°

Proceset paraprake / Prethodni procesi / Preview processes

Rasti / Slučaj / Case	ID e procesit / ID procesa / Process ID	Datë / Datum / Date
1	597	29.04.2014.

Puni / Obradio / Created: Faton.Bislimi

Nënshkrimi / Potpis / Signature:

Data/ Data/Date: 26.08.2025

Koha/ Vreme/ Time: 09:45:21

